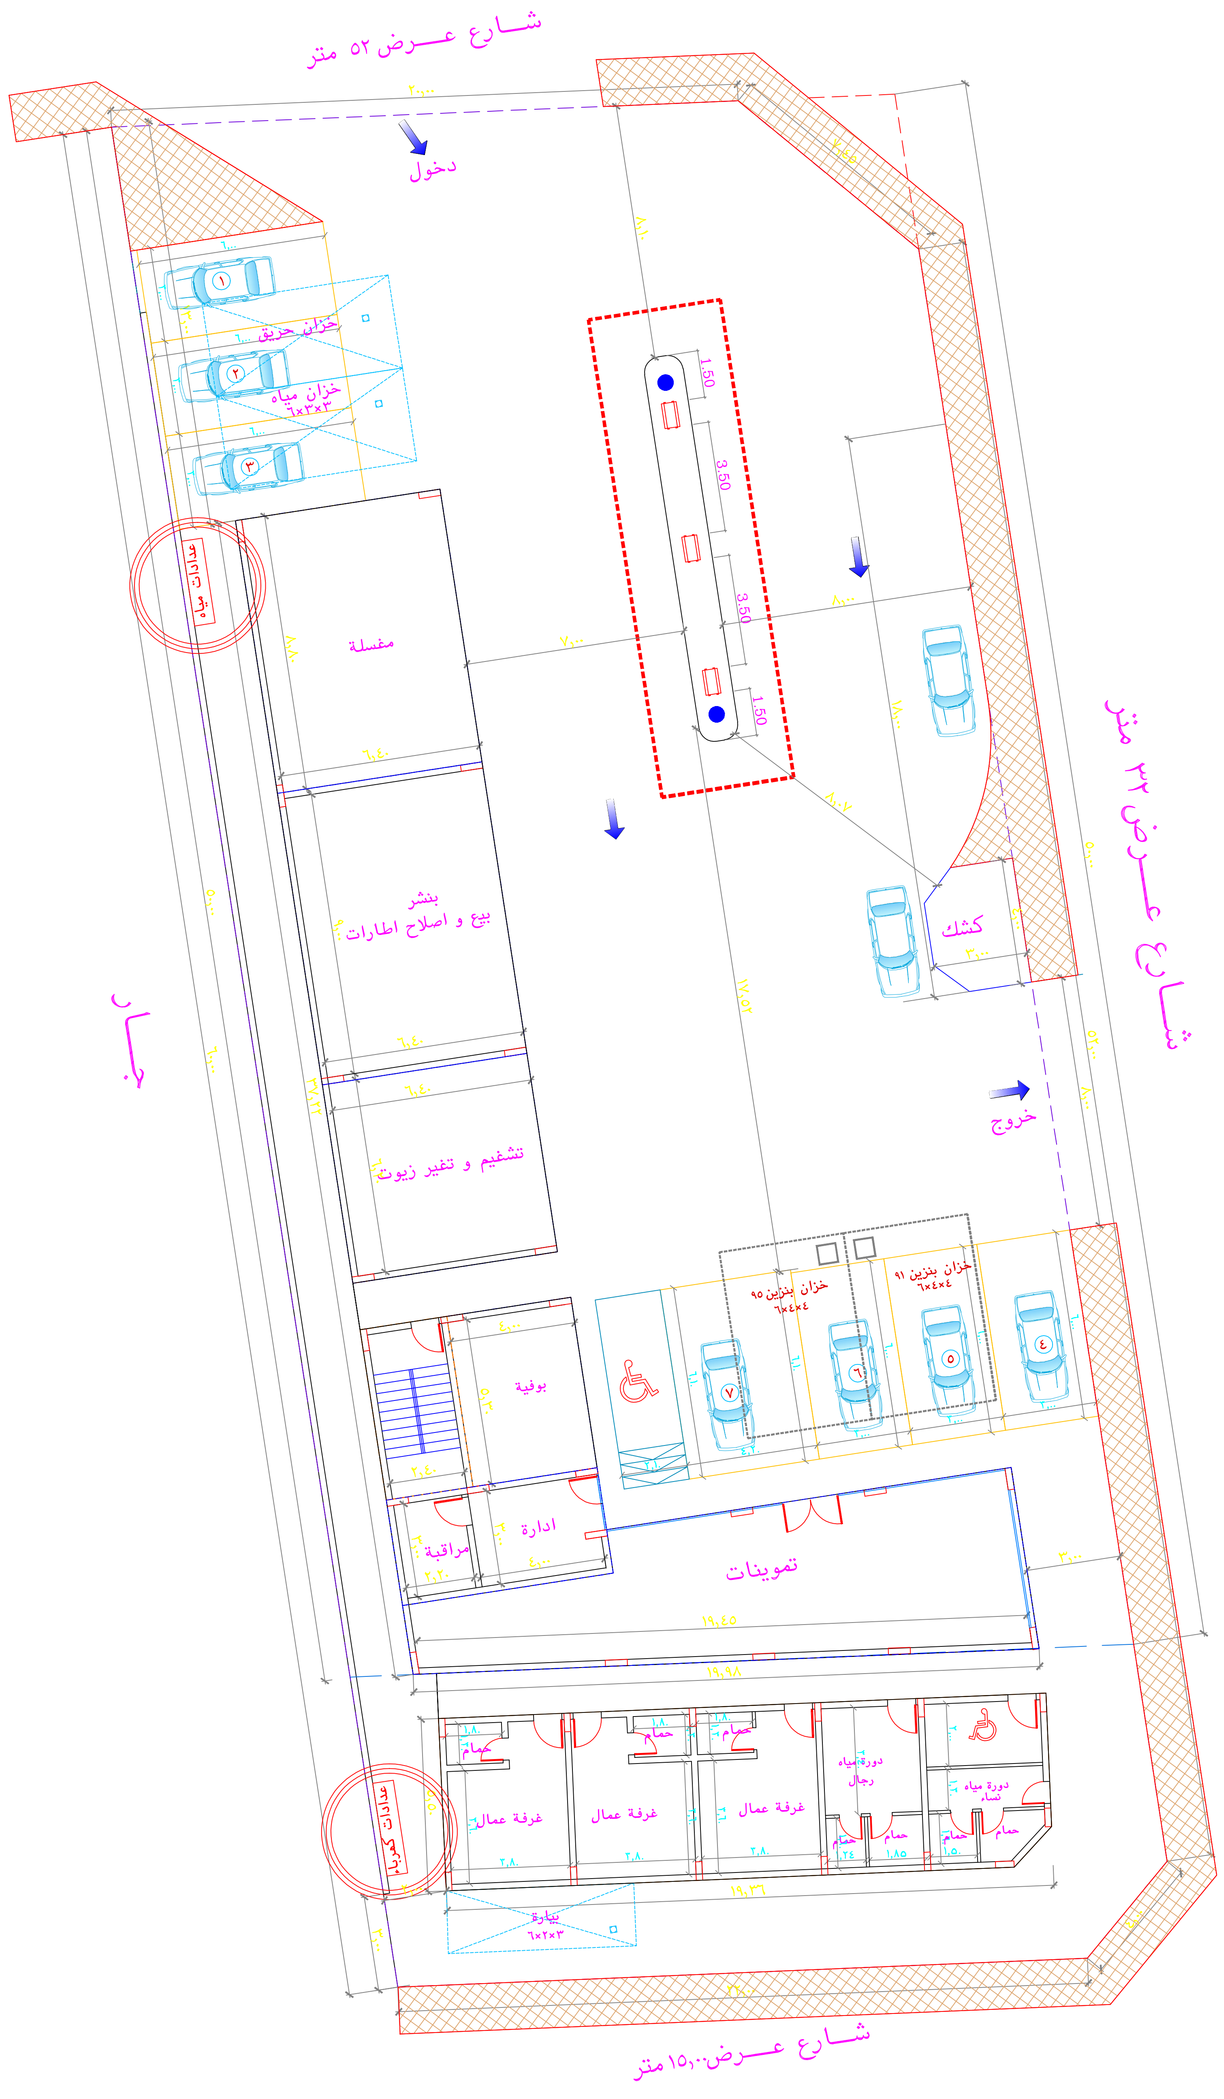

يتعهد المكتب الهندسي بان جميع التصاميم والاعمال المقدمة في هذا المشروع اعلاه
مطابقة لمتطلبات واشتراطات كود البناء السعودي الصادر بموجب قرار مجلس الوزراء
رقم ٢٤١ وتاريخ ٢٥ - ٤ - ١٤٣٨هـ والموافق عليه بالمرسوم الملكي رقم م/٣٢ وتاريخ ٢٦ - ٤ - ١٤٣٨ هـ
ويتحمل المكتب الهندسي المصمم والمكتب الهندسي المشرف على المشروع المسئولية كاملة امام الجهات
ذات العلاقة في حال مخالفة ذلك وان على المالك الالتزام بالتنفيذ بالمواد المعتمدة ضمن مواصفات ومتطلبات
واشتراطات كود البناء السعودي حيث انه لن يتم اصدار شهادة اتمام البناء الا بعد التأكد من ان جميع
المواد المستخدمة في المبنى المذكور اعلاه مطابقة لكود البناء السعودي

تتعهد بعمل اغطية خزانات التحليل (البيارات) بعمل انبوب بسقف الخزان بقطر
١٥٠ ملم لعملية شفط المياه .
- نتعهد بان تكون اغطية خزانات المياه مطابقة للمواصفات القياسية الخليجية
(GSO 2010/755)

تعهد تركيب عدادات المياه

يلزم تركيب عداد مياه لكل وحدة سكنية او تجارية
وتركيب مر شدات المياه وزنك حسب التصميم الزاري
رقم/١٨٤٤٧٤-١٨٢ بتاريخ ١٤٤٣/٠٦/٢٥ هـ
وحسب الخطاب المشار الية من شركة المياه الوطنية
برقم ١٤٤١/٥٧٢٥/٢٨٣٧ بتاريخ ١٤٤٤/٠٢/٢٤هـ
ويالتزم يتم اصدار شهادة اتمام البناءا الا بتركيب
عداد مياه لكل وحدة منفصلة

دار الاقليم
للتخطيط الحضرى والاستشارات العندسية
DAR AL EKLEM
Planning and Engineering Consultations
ترخيص (٢٥٩) ص ب ١١١١ جدة ٢١٤٣١ المملكة العربية السعودية هاتف ٠٩٦٦٢٦٨٢٢٢٨١+ فاكس ٠٩٦٦٢٦٨٢٢٢٨٧+

المشروع محطة وقود	ملك فـهد محمد حسن الزهراني	ختم
اسم الوحه معمـــاري	مسقط الافقـي الدور الارضى	التوقيع
لوحه رقـم ٢	معندس معمارى	مقياس الرسم ١-٢٠٠